



Útgáfa	Lýsing	Dags.
-		
-		

The figure consists of two horizontal lines. The upper line is dashed and labeled "Järn í efri brún". The lower line is solid and labeled "Järn í neðri brún". Both lines extend from the left side of the graph towards the right. A vertical dashed line is positioned at the year 1000 on the x-axis.

Horft upp undir svalir

K10 c/c 200
L=4550

K10 c/c 200
L=4450

K12 c/c 150
K10 c/c 200
L=3500
L=2300

Útbrún svala:
U-lykkjur K10 c/c 200
L=500+Mælist+500
2 K12 í lykkiuhorn

The technical drawing illustrates a duct system with the following details:

- Horizontal Duct:** A long horizontal duct section with a thickness of $t = 180$. It features a vertical support leg at the bottom left labeled "Halli" with a thickness of $t = 200$.
- Vertical Duct:** A vertical duct section on the right with a total height of 1835. It has a top cap labeled "SV1 BS-01".
- Bottom Duct:** A horizontal duct section at the bottom with a thickness of $t = 180$. It has a top cap labeled "SV4 BS-01".
- Bottom Support:** A horizontal support bar at the bottom with a thickness of $t = 100$. It has a top cap labeled "SV3 BS-01".
- Vertical Support:** A vertical support leg on the left side of the bottom duct, labeled "Halli" with a thickness of $t = 200$.
- Annotations:** The text "050 innsteyppt rör halli um 15mm/m frá niðurfalli" is present, indicating a slope of 15 mm per meter downwards from the top.
- Dimensions:** Vertical dimensions include 100 at the top of the vertical duct, 1735 for the total height of the vertical duct, and 1835 for its total length. Horizontal dimensions include 180 for the thickness of the horizontal ducts and 100 for the thickness of the bottom support.

Skýringar:
Á teikningu B-01 eru almennar skýringar og öll lágmarks ákvæði varðandi steypu og bendistál t.d. frágangur á járnum kringum op og brúnir og fl.



Um nákvæma stærð og staðsetningu einstakra byggingahluta. Sjá nánar á sérteikningum aðalhönnuðar.

Göt og raufar (sjá lagnateikn.)

ATH!
VARÐANDI STEYPUHULU SJÁ NÁNAR Á
SKÝRINGABLAÐI B01.

**ALLAR SVALAPLÖTUR SKULU STEYPTAR MED
C30/37 STEINSTEYPU MED ÞÉTTUM
FYLLIEFNUM !**

ATH!
ÖLL MÁL SKULU YFIRFARIN GAUMGÆFILEGA
ÁDUR EN FRAMKVÆMDIR HEFJAST.

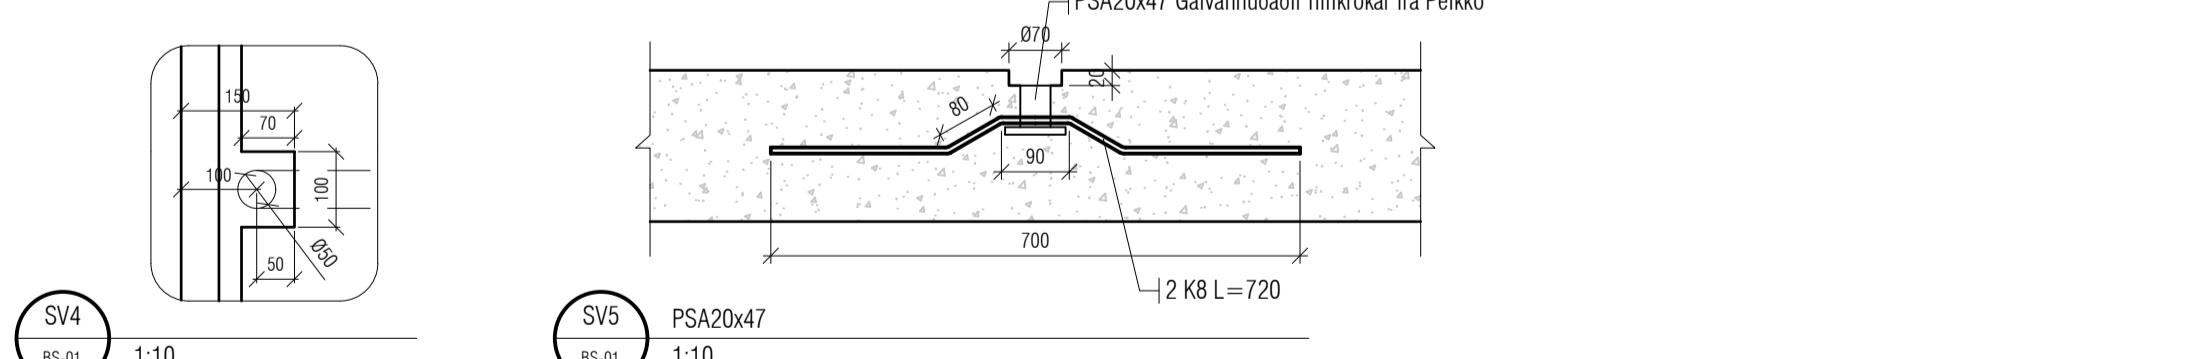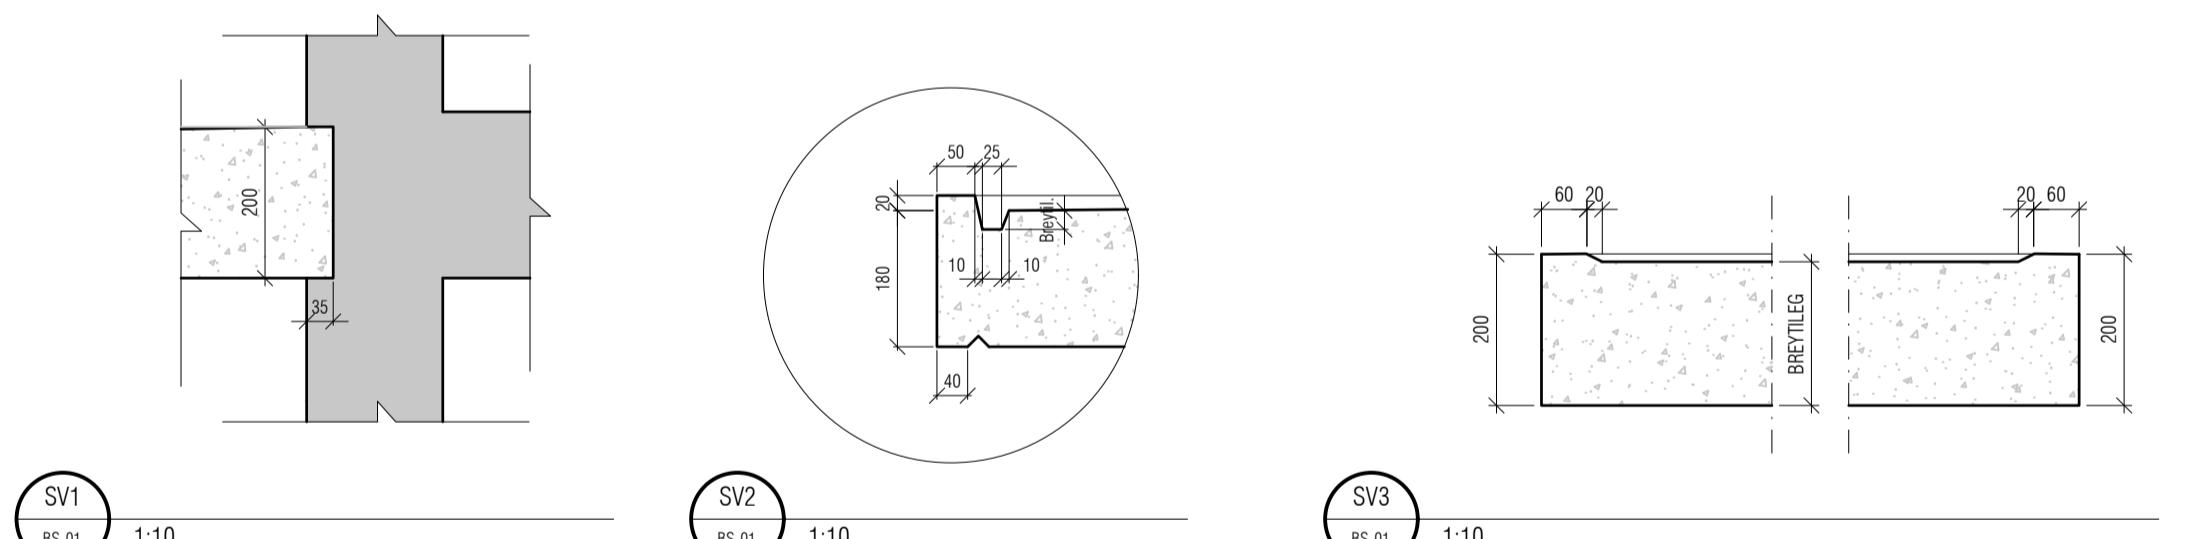

Áshamar 54 - Hafnarfjörður

Þateikning - Grunnmyndir og deili		
SH/ÖJH	Teiknað	Teikn. nr.
g 10.05.2022	Mkv. 1:50	BS_01
Hafsteinsson kt. 030859-7749		
Atæknifraeðingur		
Götuvegur		

aðalhöppuðar / samræmingarhöppuðar: